

PRICE SCOPE: only the Nudura ICF formwork and associated accessories are included in our price. All other structure and information shown is supplied in good faith for coordination only and must be checked by the relevant professional.

QUOTATION - NOT FOR CONSTRUCTION

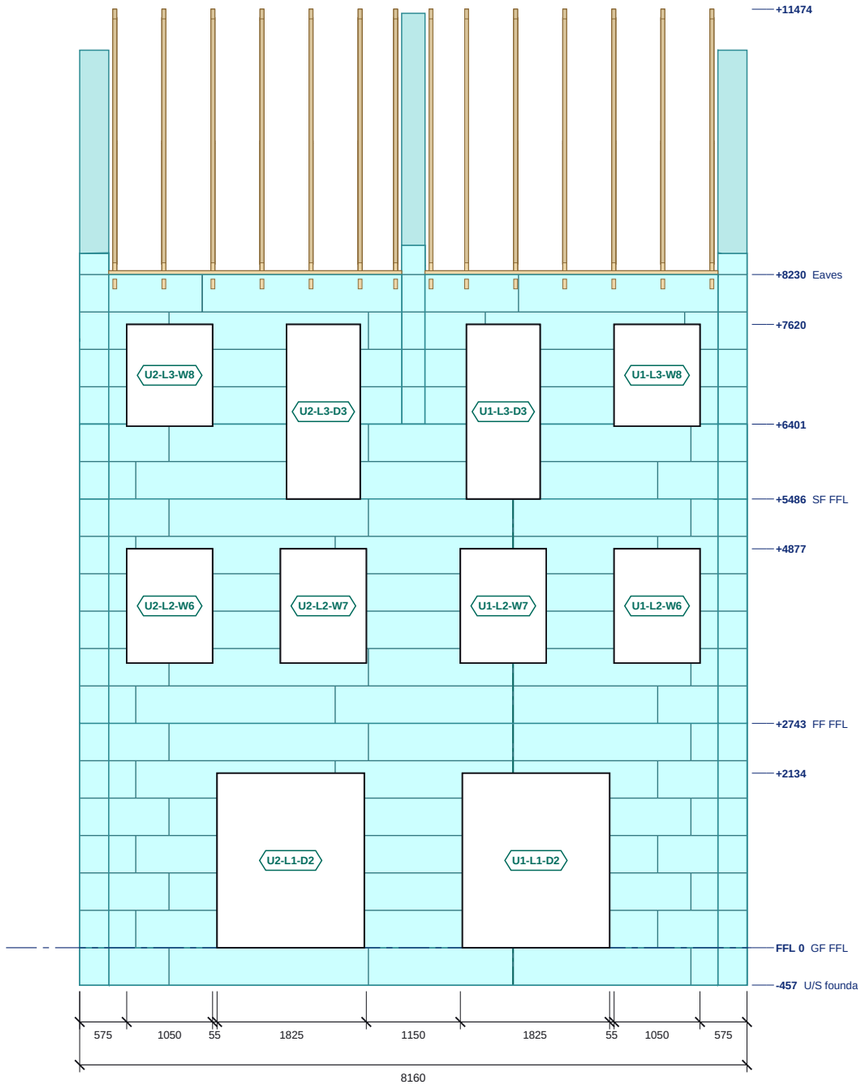

REAR ELEVATION

Scale 1:75 @ A3 | Levels above GF FFL; sills and heads in the schedule

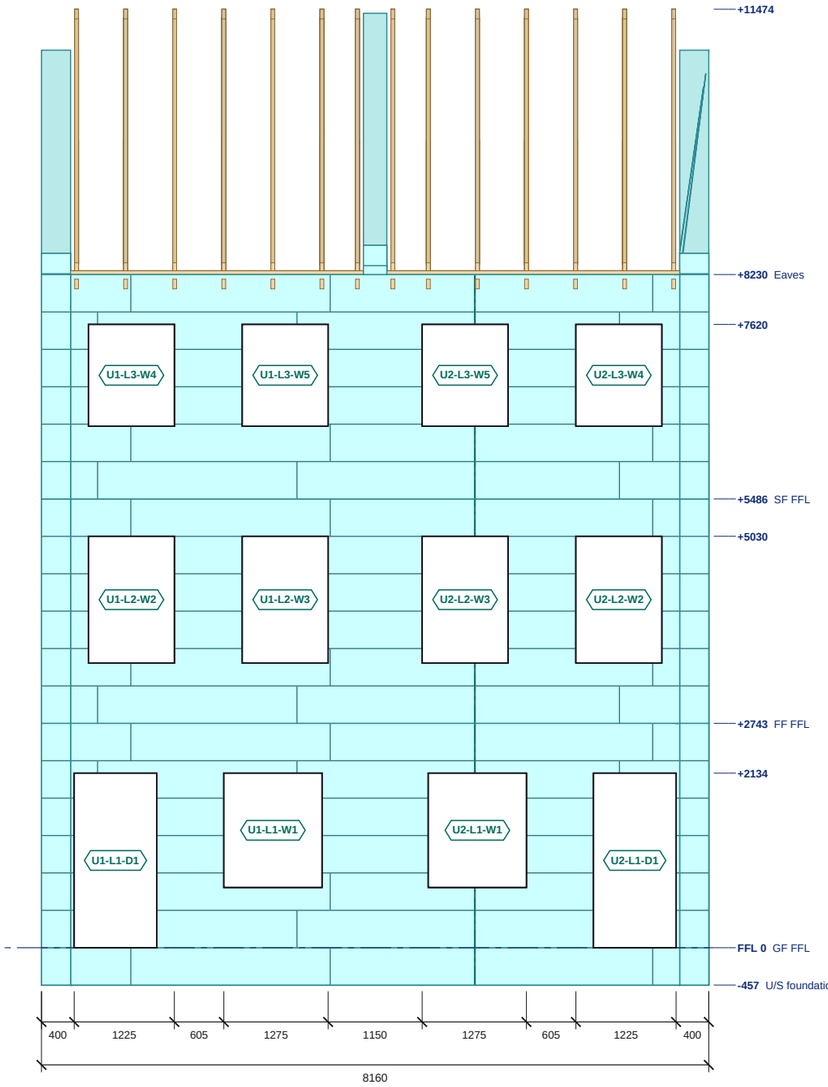

FRONT ELEVATION

Scale 1:75 @ A3 | Levels above GF FFL; sills and heads in the schedule

0 1 2 3 4m

ICF external EPS face
Block course joint
Stack joint

Do not scale. All dimensions in millimetres, levels in metres from GF FFL. Check all dimensions on site.

ELEVATION SCHEDULES

REAR ELEVATION: OPENINGS

Ref	Width	Height	Sill	Head	Lintel
U1-L1-D2	1800	2134	0	+2134	-
U1-L2-W6	1050	1397	+3480	+4877	-
U1-L2-W7	1050	1397	+3480	+4877	-
U1-L3-W8	1050	1244	+6376	+7620	-
U1-L3-D3	900	2134	+5486	+7620	-
U2-L1-D2	1800	2134	0	+2134	-
U2-L2-W6	1050	1397	+3480	+4877	-
U2-L2-W7	1050	1397	+3480	+4877	-
U2-L3-W8	1050	1244	+6376	+7620	-
U2-L3-D3	900	2134	+5486	+7620	-

Structural openings in the ICF; sill and head above GF FFL.

FRONT ELEVATION: OPENINGS

Ref	Width	Height	Sill	Head	Lintel
U1-L1-D1	1010	2134	0	+2134	-
U1-L1-W1	1200	1397	+737	+2134	-
U1-L2-W2	1050	1549	+3480	+5029	-
U1-L2-W3	1050	1549	+3480	+5029	-
U1-L3-W4	1050	1244	+6376	+7620	-
U1-L3-W5	1050	1244	+6376	+7620	-
U2-L1-D1	1010	2134	0	+2134	-
U2-L1-W1	1200	1397	+737	+2134	-
U2-L2-W2	1050	1549	+3480	+5029	-
U2-L2-W3	1050	1549	+3480	+5029	-
U2-L3-W4	1050	1244	+6376	+7620	-
U2-L3-W5	1050	1244	+6376	+7620	-

Structural openings in the ICF; sill and head above GF FFL.

LEVELS ON THESE ELEVATIONS

Level	FFL
U/S foundation ICF	-457
GF FFL	0
top of ICF	+2134
FF FFL	+2743
top of ICF	+4877
top of ICF	+5030
SF FFL	+5486
top of ICF	+6401
top of ICF	+7620
Eaves	+8230
top of roof build-up	+11474

NOTES

1. ICF: Nudura 6" XR35, 101.6 EPS + 152.4 core + 101.6 EPS = 355.6; 6" Std, 66.7 EPS + 152.4 core + 66.7 EPS = 285.8. External EPS face shown with the block course joints, vertical block joints and stack joints as populated.
2. Levels above GF FFL. Openings are structural openings in the ICF; glazing, doors, render and finishes by others, not shown.
3. ICF walls as modelled.
4. See ES26-064-GA-01 for plan setting out, lintels and steel.

REVISIONS

REV	DATE	DESCRIPTION
-	10.11.26	Quotation issue

Nudura™ BuildEase

CLIENT	PROJECT
Cuckfield Real Estate Ltd	Redcatch Quarter, Knowle, Bristol

DRAWING TITLE

NORTH AND SOUTH ELEVATIONS

ICF elevations with openings, levels and roof build-up

SCALE	SIZE	DATE
1:75	A3	10.11.26
DRAWN	CHECKED	APPROVED
TS		

STATUS	DRAWING No.	REV
QUOTATION	ES26-064-EL-01	-